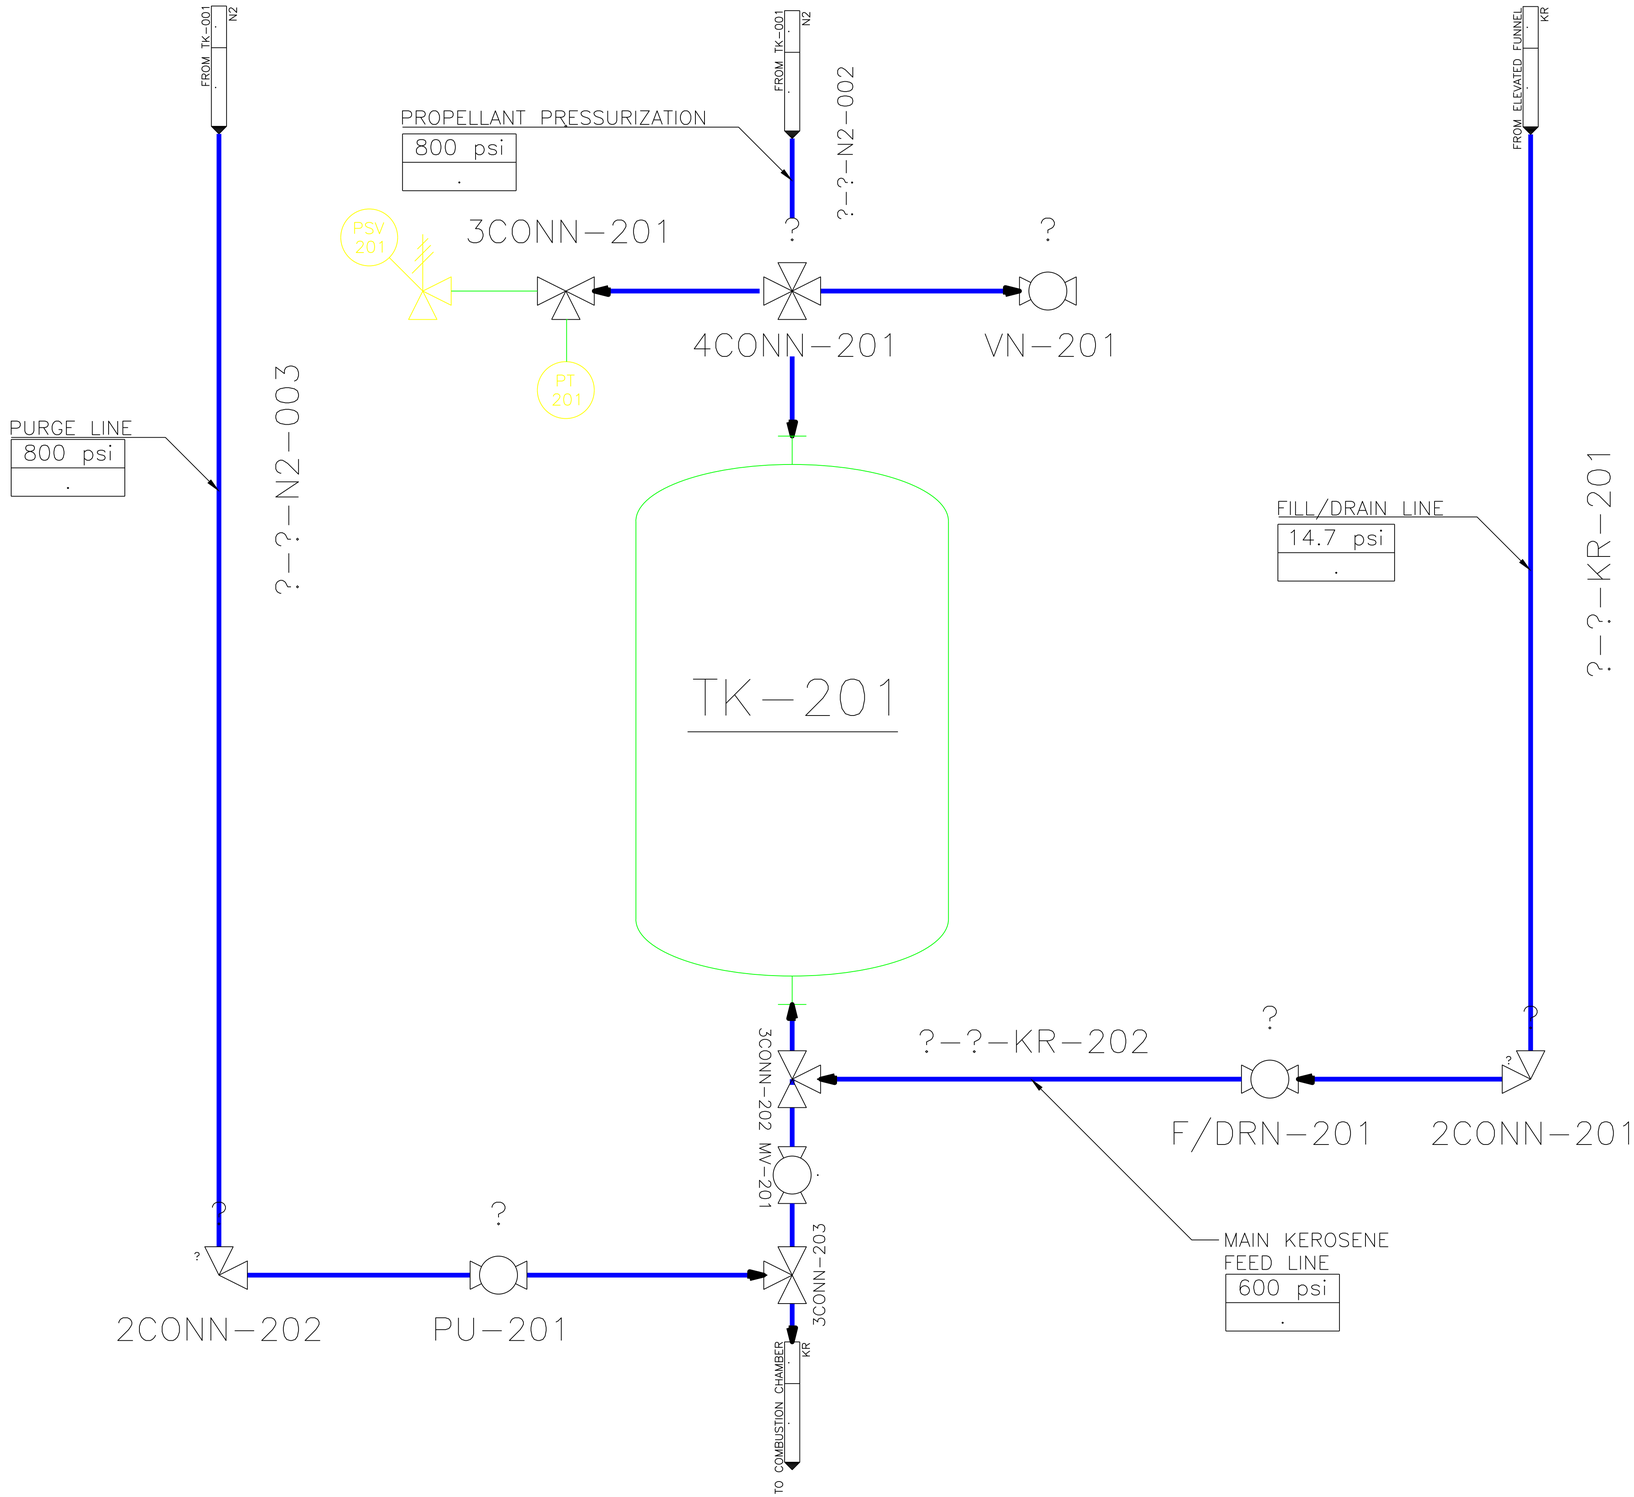

General Notes

No.	Revision/Issue	Date

Drawing Name
Kerosene Feed Line
####

Project Name and Address
Project 6

---- ----

Area
####

Drawing Number
####

Author
Wilson Li

Stamp

D:\GitHub\APL\Mu-Propellant-Feed\Engine mu P&ID\P&ID DWG\Kerosene Line.dwg